
ESQUEMA UNIFILAR -UNA VIVIENDA (115 m2)

(Las dos viviendas son en espeja y cuentan con medidores independientes)

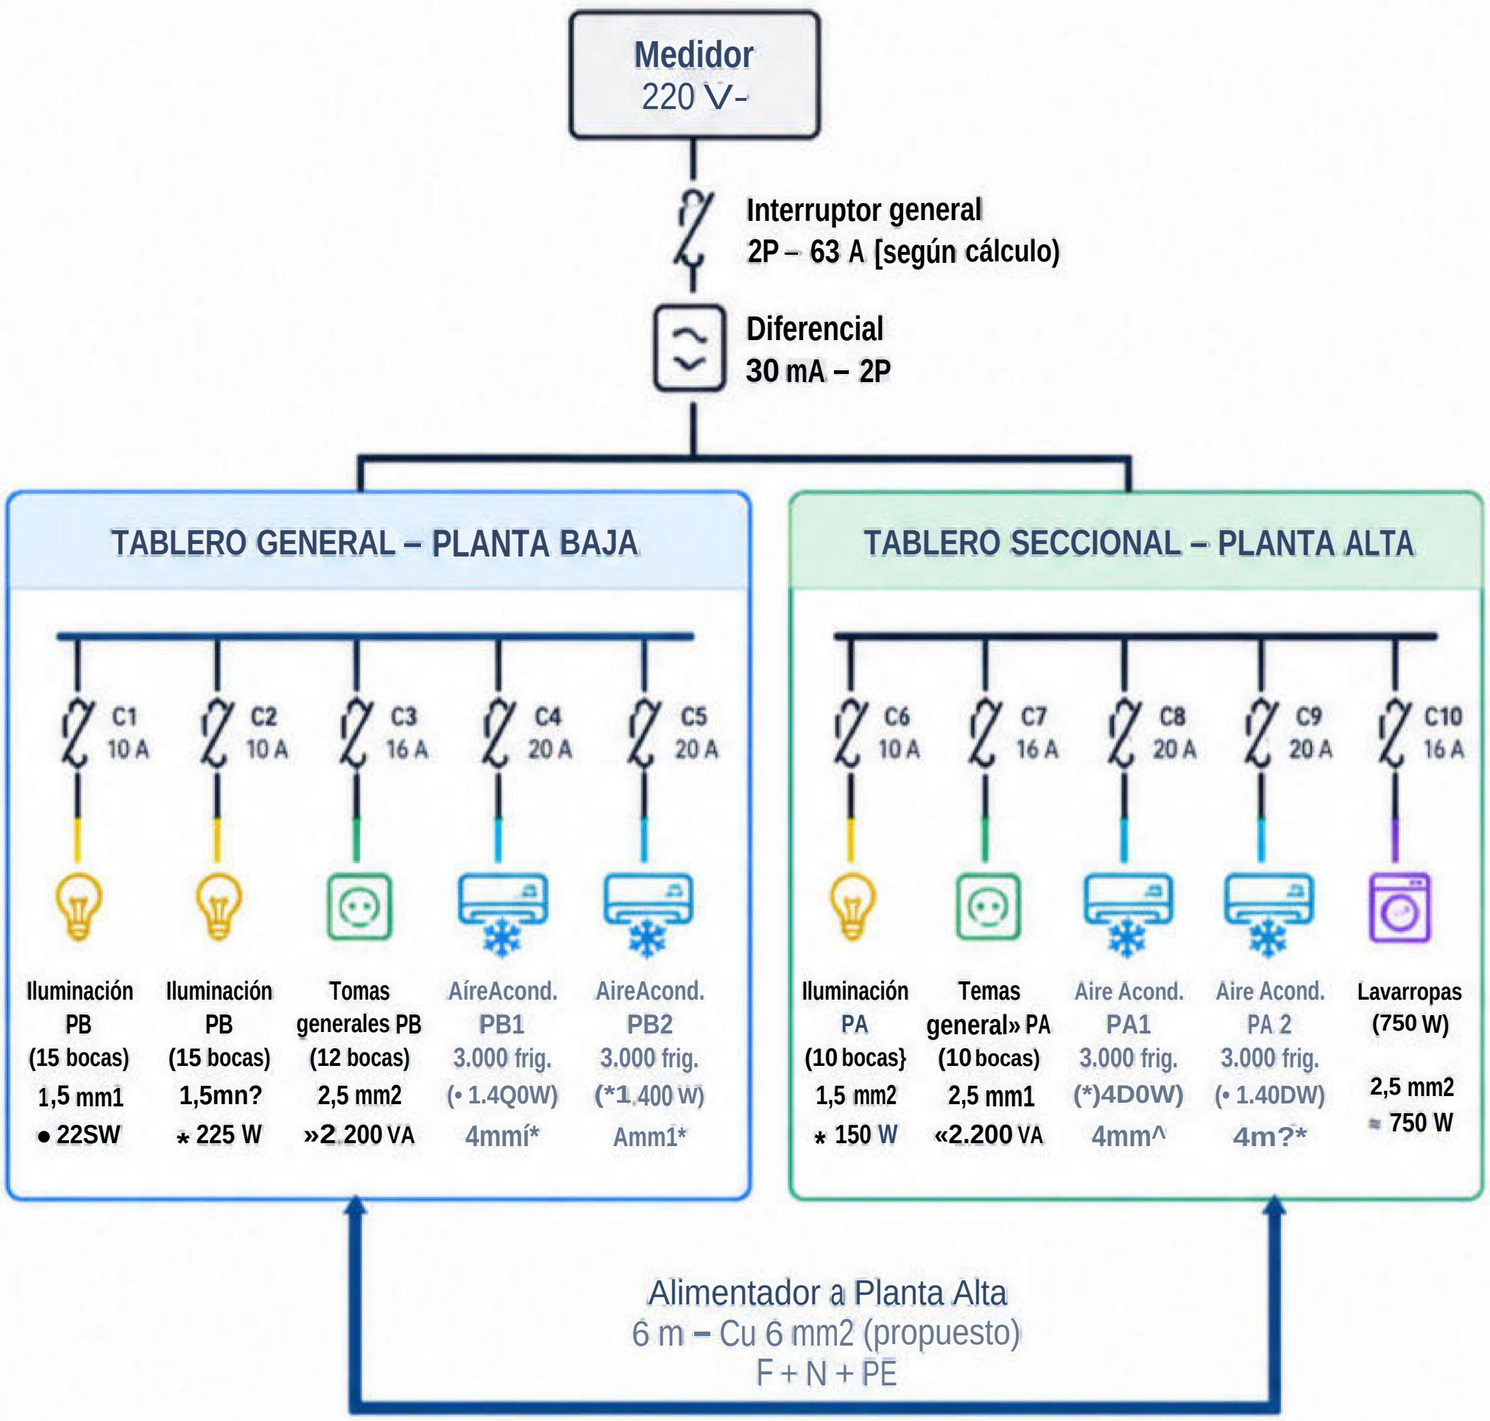

CUADRO DE CIRCUITOS Y POTENCIAS (una vivienda)

N° Circurto	Descripción	Cant	Pot. unitaria (W)	Pot. total (W)	Corriente (A) = 220V
PLANTA BAJA					
C1	Humillación PB	15 bocas	15	225	LO
C2	Iluminación PB	15 bocas	15	225	LO
C3	Tomas generales PB	12 bocas	2.200	2.200	10,0
04	Aire acondicionado PB 1	1	1.400	1.400	6,4
C5	Aire acondicionado PB 2	1	1.400	1.400	6,4
Subtotal PB				**6*450**	**29,3**
PLANTA ALTA					
C6	Iluminación PA	10 bocas	15	150	07
C7	Tomas generales PA	10 bocas	2.200	2.200	10,0
ca	Aire acondicionado PA 1	1	1.400	1.400	6,4
C9	Aire acondicionado PA 2	1	1.400	1.400	6,4
C10	Lavarropas	1	750	750	3,4
Subtotal PA				**5.900**	**27,0**
Total vivienda [sin considerar fomacorrientes generales adicionales ni otros equipos)				**12.350 W ≈ 56,3 A**	

Referencias del unifilar

- Medidor
- Interruptor general / termomagnética
- Diferencial 30 mA
- Alimentador 3 planta alta

Colores de circuitos

- Iluminación
- Tomas generales
- Aires acondicionados
- Lavañopas

• Secctón orientaría. Debe verificarse *por corriente admisible, caída de tensión y método de instalación.*

Notas importantes

i. La potencia de los aires acondicionados (1.400 W c/u) es una estimación conservadora. Debe verificarse la potencia de placa de cada equipo.

2. La demanda final debe calcularse según AEA 90364-7-770 (grado de electrificación, coeficientes de simultaneidad, etc.),

3. Se recomienda consultar a la distribuidora la factibilidad de un suministro 1rifasico (para cargas ⁎ 7 kVA o > 32 A en monofásico).

4. Las secciones de conductores y las protecciones definitivas deben verificarse según método de instalación, agruparaiento y condiciones de obra.

5. La instalación debe ser ejecutada por un Instalador Electricista Habilitado y certificada según la Ley Provincial 10.281 y la reglamentación vigente.